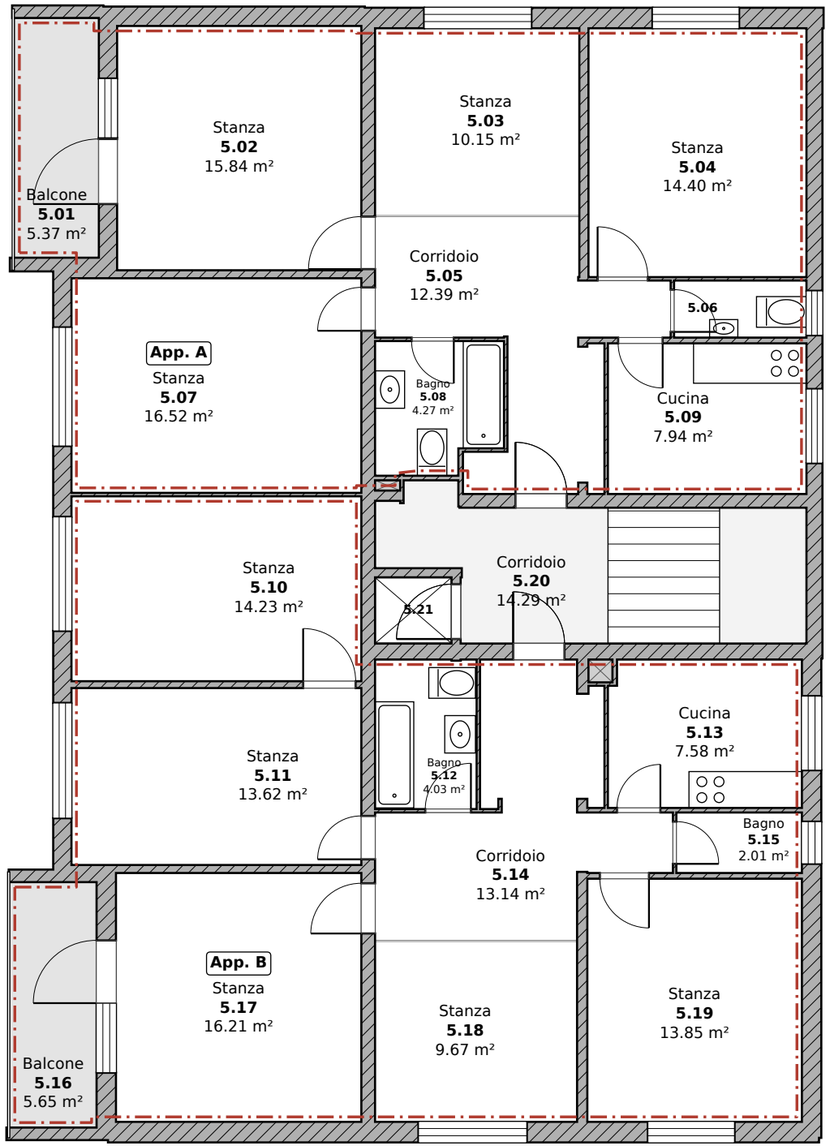

Legenda

- WC
- Lavabo
- Vasca da bagno
- Doccia
- Blocco cucina
- Lavatrice
- Porta
- Finestra

N

0 1 2 5 m

Scala 1:100

Confine dell'unità

Progetto	Site 1102 · Edificio 2242
Disegno	**Pianta 5° piano**
Scala	1:100 (A3)
N. disegno	2242-10281
	Misure in metri · Superfici: superfici nette in m²

Source: Swiss Dwellings v3.0.0, Archilyse AG (doi:10.5281/zenodo.7788422), CC BY 4.0.
Rendered from the dataset geometry; label language and numbering are synthetic.